
ENACOPOL ANDONI-RAZVAN
2025.12.23 10:42

Arie construită
ETAJ
A: 149.08 m²
V: 447.78 m³

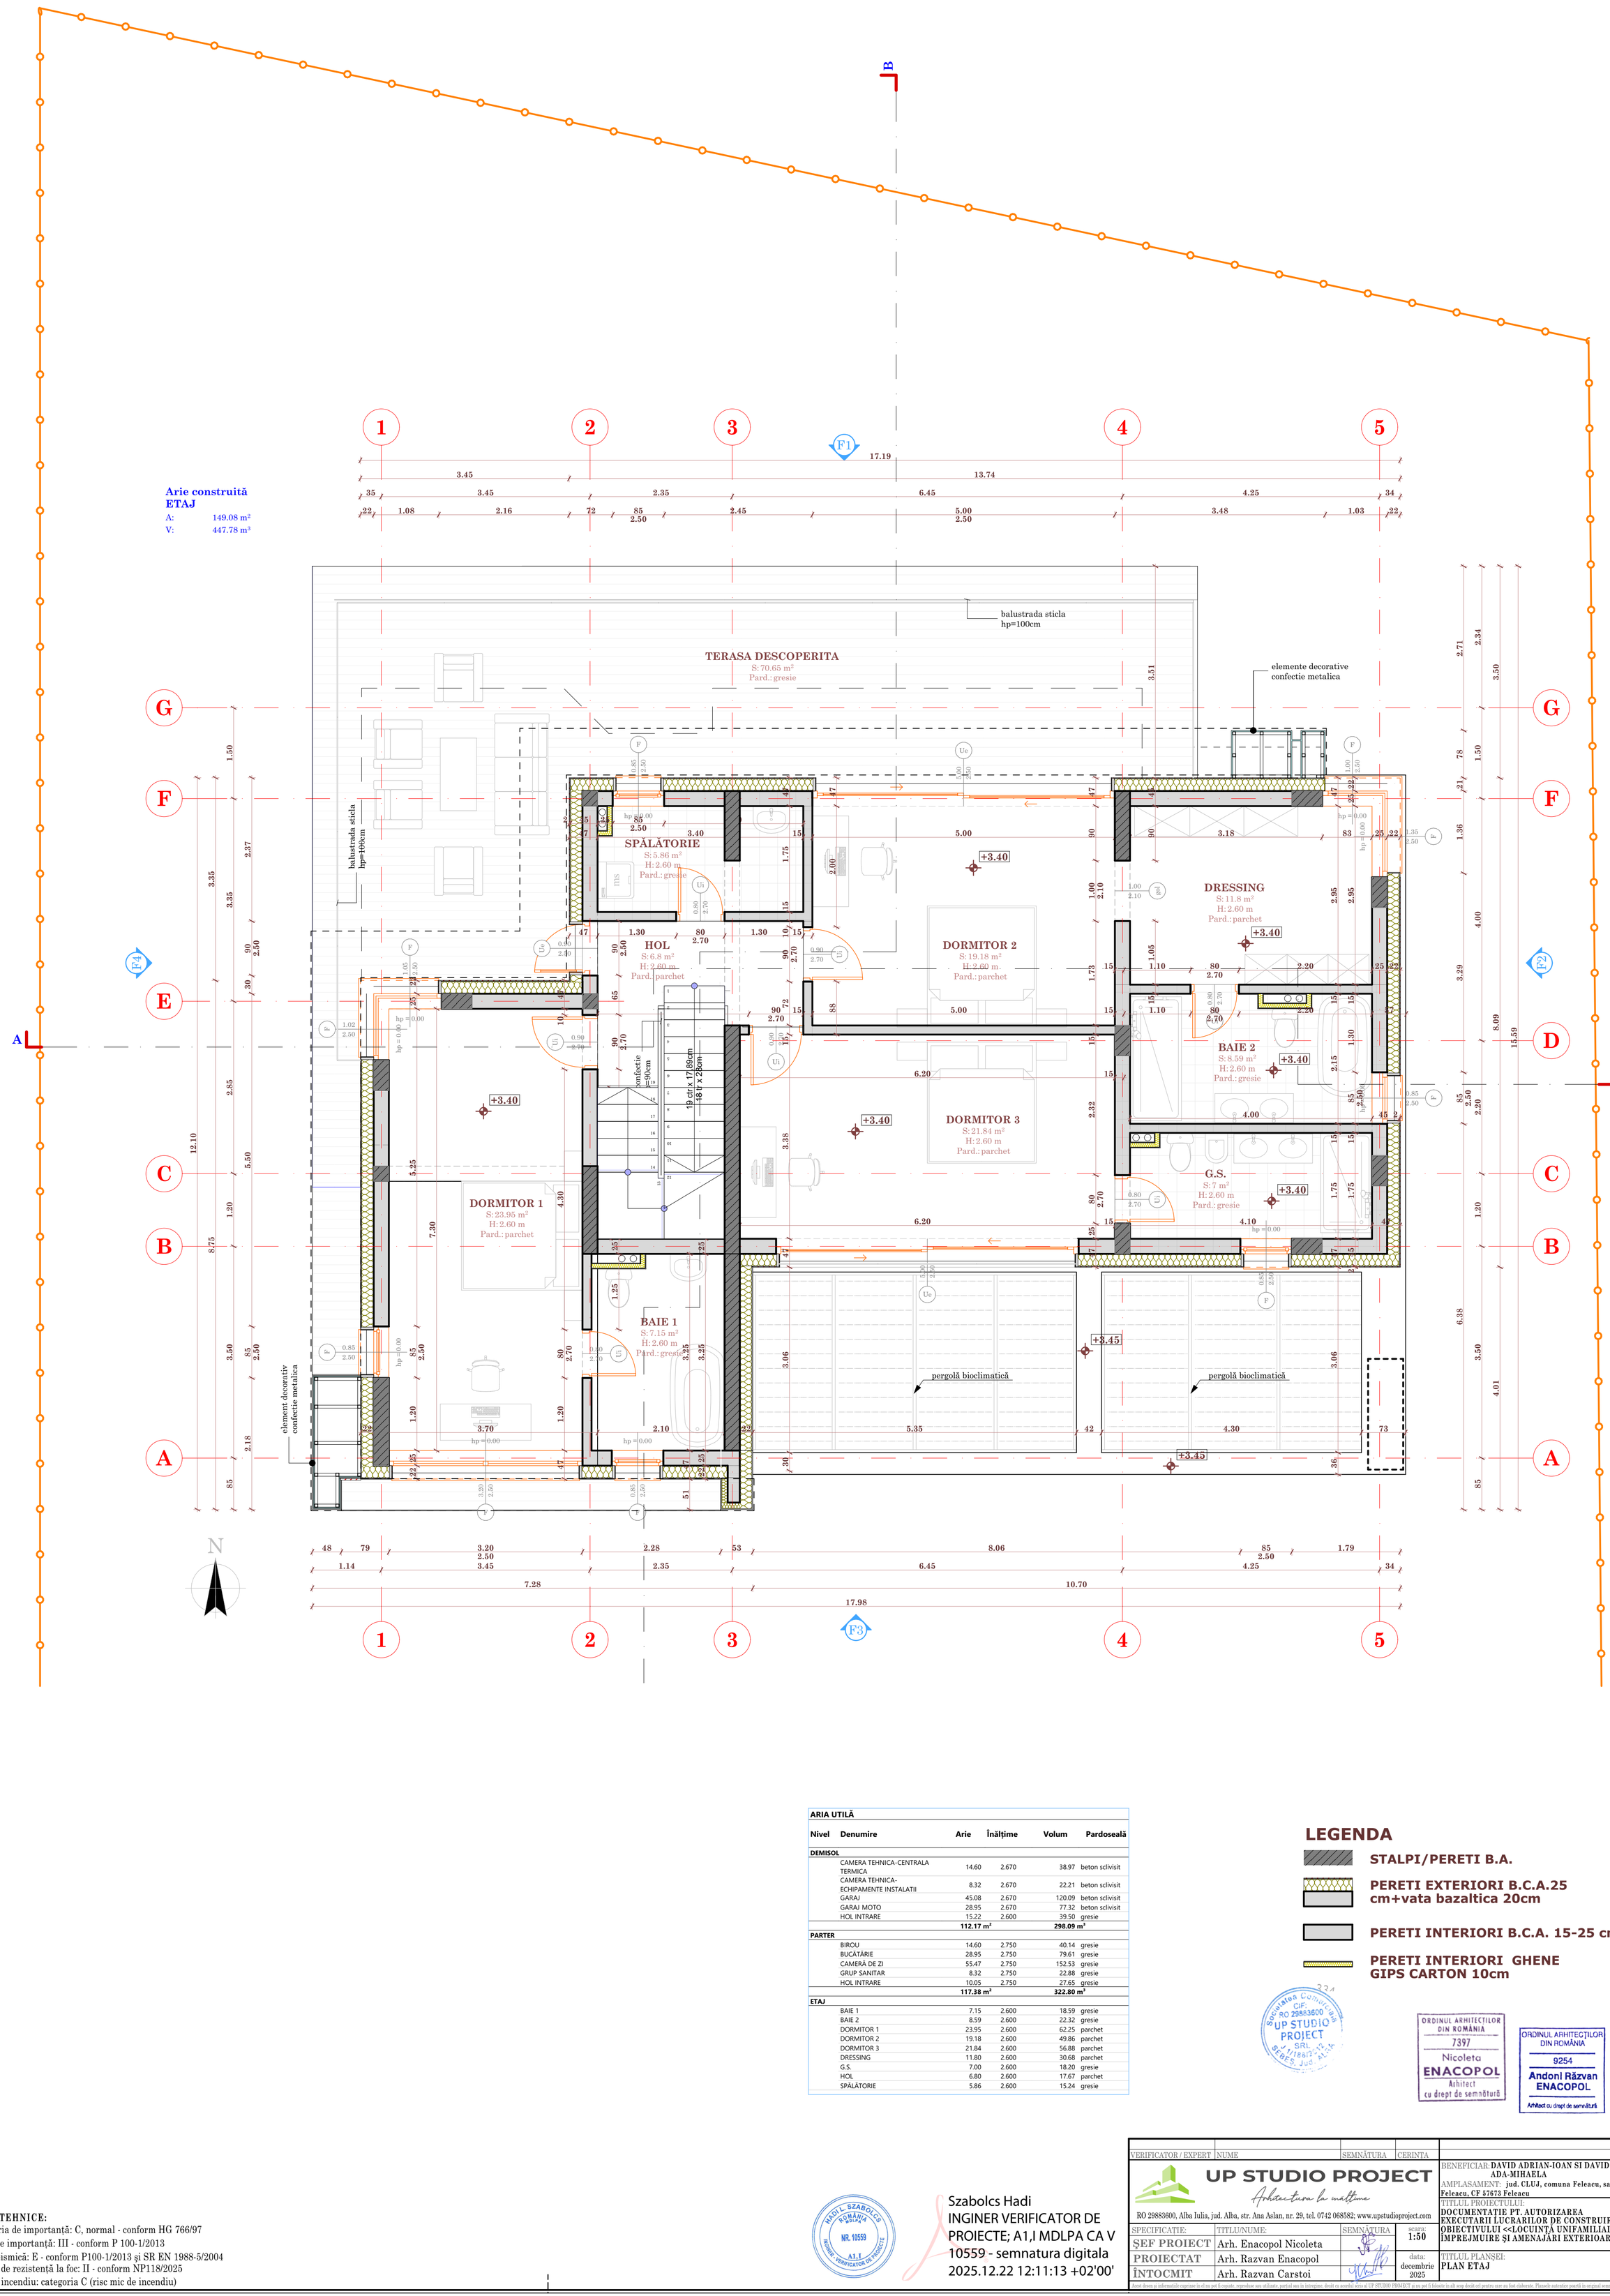

ARIA UTILĂ					
Nivel	**Denumire**	**Arie**	**Înălțime**	**Volum**	**Pardoseală**
DEMISOL					
	CAMERA TEHNICA-CENTRALA TERMICA	14.60	2.670	38.97	beton sclivisit
	CAMERA TEHNICA-ECHIPAMENTE INSTALATII	8.32	2.670	22.21	beton sclivisit
	GARAJ	45.08	2.670	120.09	beton sclivisit
	GARAJ MOTO	28.95	2.670	77.32	beton sclivisit
	HOL INTRARE	15.22	2.600	39.50	gresie
		112.17 m²		**298.09 m³**	
PARTER					
	BIROU	14.60	2.750	40.14	gresie
	BUCĂTĂRIE	28.95	2.750	79.61	gresie
	CAMERĂ DE ZI	55.47	2.750	152.53	gresie
	GRUP SANITAR	8.32	2.750	22.88	gresie
	HOL INTRARE	10.05	2.750	27.65	gresie
		117.38 m²		**322.80 m³**	
ETAJ					
	BAIE 1	7.15	2.600	18.59	gresie
	BAIE 2	8.59	2.600	22.32	gresie
	DORMITOR 1	23.95	2.600	62.25	parchet
	DORMITOR 2	19.18	2.600	49.86	parchet
	DORMITOR 3	21.84	2.600	56.88	parchet
	DRESSING	11.80	2.600	30.68	parchet
	G.S.	7.00	2.600	18.20	gresie
	HOL	6.80	2.600	17.67	parchet
	SPĂLĂTORIE	5.86	2.600	15.24	gresie

LEGENDA

- STALPI/PERETI B.A.
- PERETI EXTERIORI B.C.A.25 cm+vata bazaltica 20cm
- PERETI INTERIORI B.C.A. 15-25 cm
- PERETI INTERIORI GHENE GIPS CARTON 10cm

DATE TEHNICE:
Categoria de importanță: C, normal - conform HG 766/97
Clasa de importanță: III - conform P 100-1/2013
Zona seismică: E - conform P100-1/2013 şi SR EN 1988-5/2004
Gradul de rezistență la foc: II - conform NP118/2025
Risc de incendiu: categoria C (risc mic de incendiu)

Szabolcs Hadi
INGINER VERIFICATOR DE PROIECTE; A1,I MDLPA CA V 10559 - semnatura digitala
2025.12.22 12:11:13 +02'00'

VERIFICATOR / EXPERT	NUME	SEMNĂTURA	CERINȚA

UP STUDIO PROJECT
Arhitectura la maxim
RO 29883600, Alba Iulia, jud. Alba, str. Ana Aslan, nr. 29, tel. 0742 068582; www.upstudioproject.com

SPECIFICAȚIE:	TITLU/NUME:	SEMNĂTURA	scara: 1:50
ŞEF PROIECT	Arh. Enacopol Nicoleta		
PROIECTAT	Arh. Razvan Enacopol		data: decembrie 2025
ÎNTOCMIT	Arh. Razvan Carstoi		

BENEFICIAR: **DAVID ADRIAN-IOAN SI DAVID ADA-MIHAELA**
AMPLASAMENT: **jud. CLUJ, comuna Feleacu, sat Feleacu, CF 57673 Feleacu**
TITLUL PROIECTULUI: **DOCUMENTAȚIE PT. AUTORIZAREA EXECUTARII LUCRARILOR DE CONSTRUIRE A OBIECTIVULUI <<LOCUINȚĂ UNIFAMILIALĂ ÎMPREJMUIRE ŞI AMENAJĂRI EXTERIOARE>>**
TITLUL PLANŞEI: **PLAN ETAJ**

project nr.: **245/2024**
faza:
format: **A1** (84.1 x 59.1 cm)
planșa nr.: **A04**

Acest desen și informațiile conținute în el nu pot fi copiate, reproduse sau utilizate, parțial sau în întregime, decât cu acordul scris al UP STUDIO PROJECT și nu pot fi folosite în alt scop decât cel pentru care au fost elaborate. Planele autentice poartă în original semnătura și ștampila UP STUDIO PROJECT