
CLAUDIU-DANIEL SALANTA
Arhitect Sef
Data: 14/4/2026 Ora: 13:26
Motiv: Eliberare document

ENACOPOL ANDONI RAZVAN
2026.02.24 15:13

Nr. inregistrare 163/17.03.2026

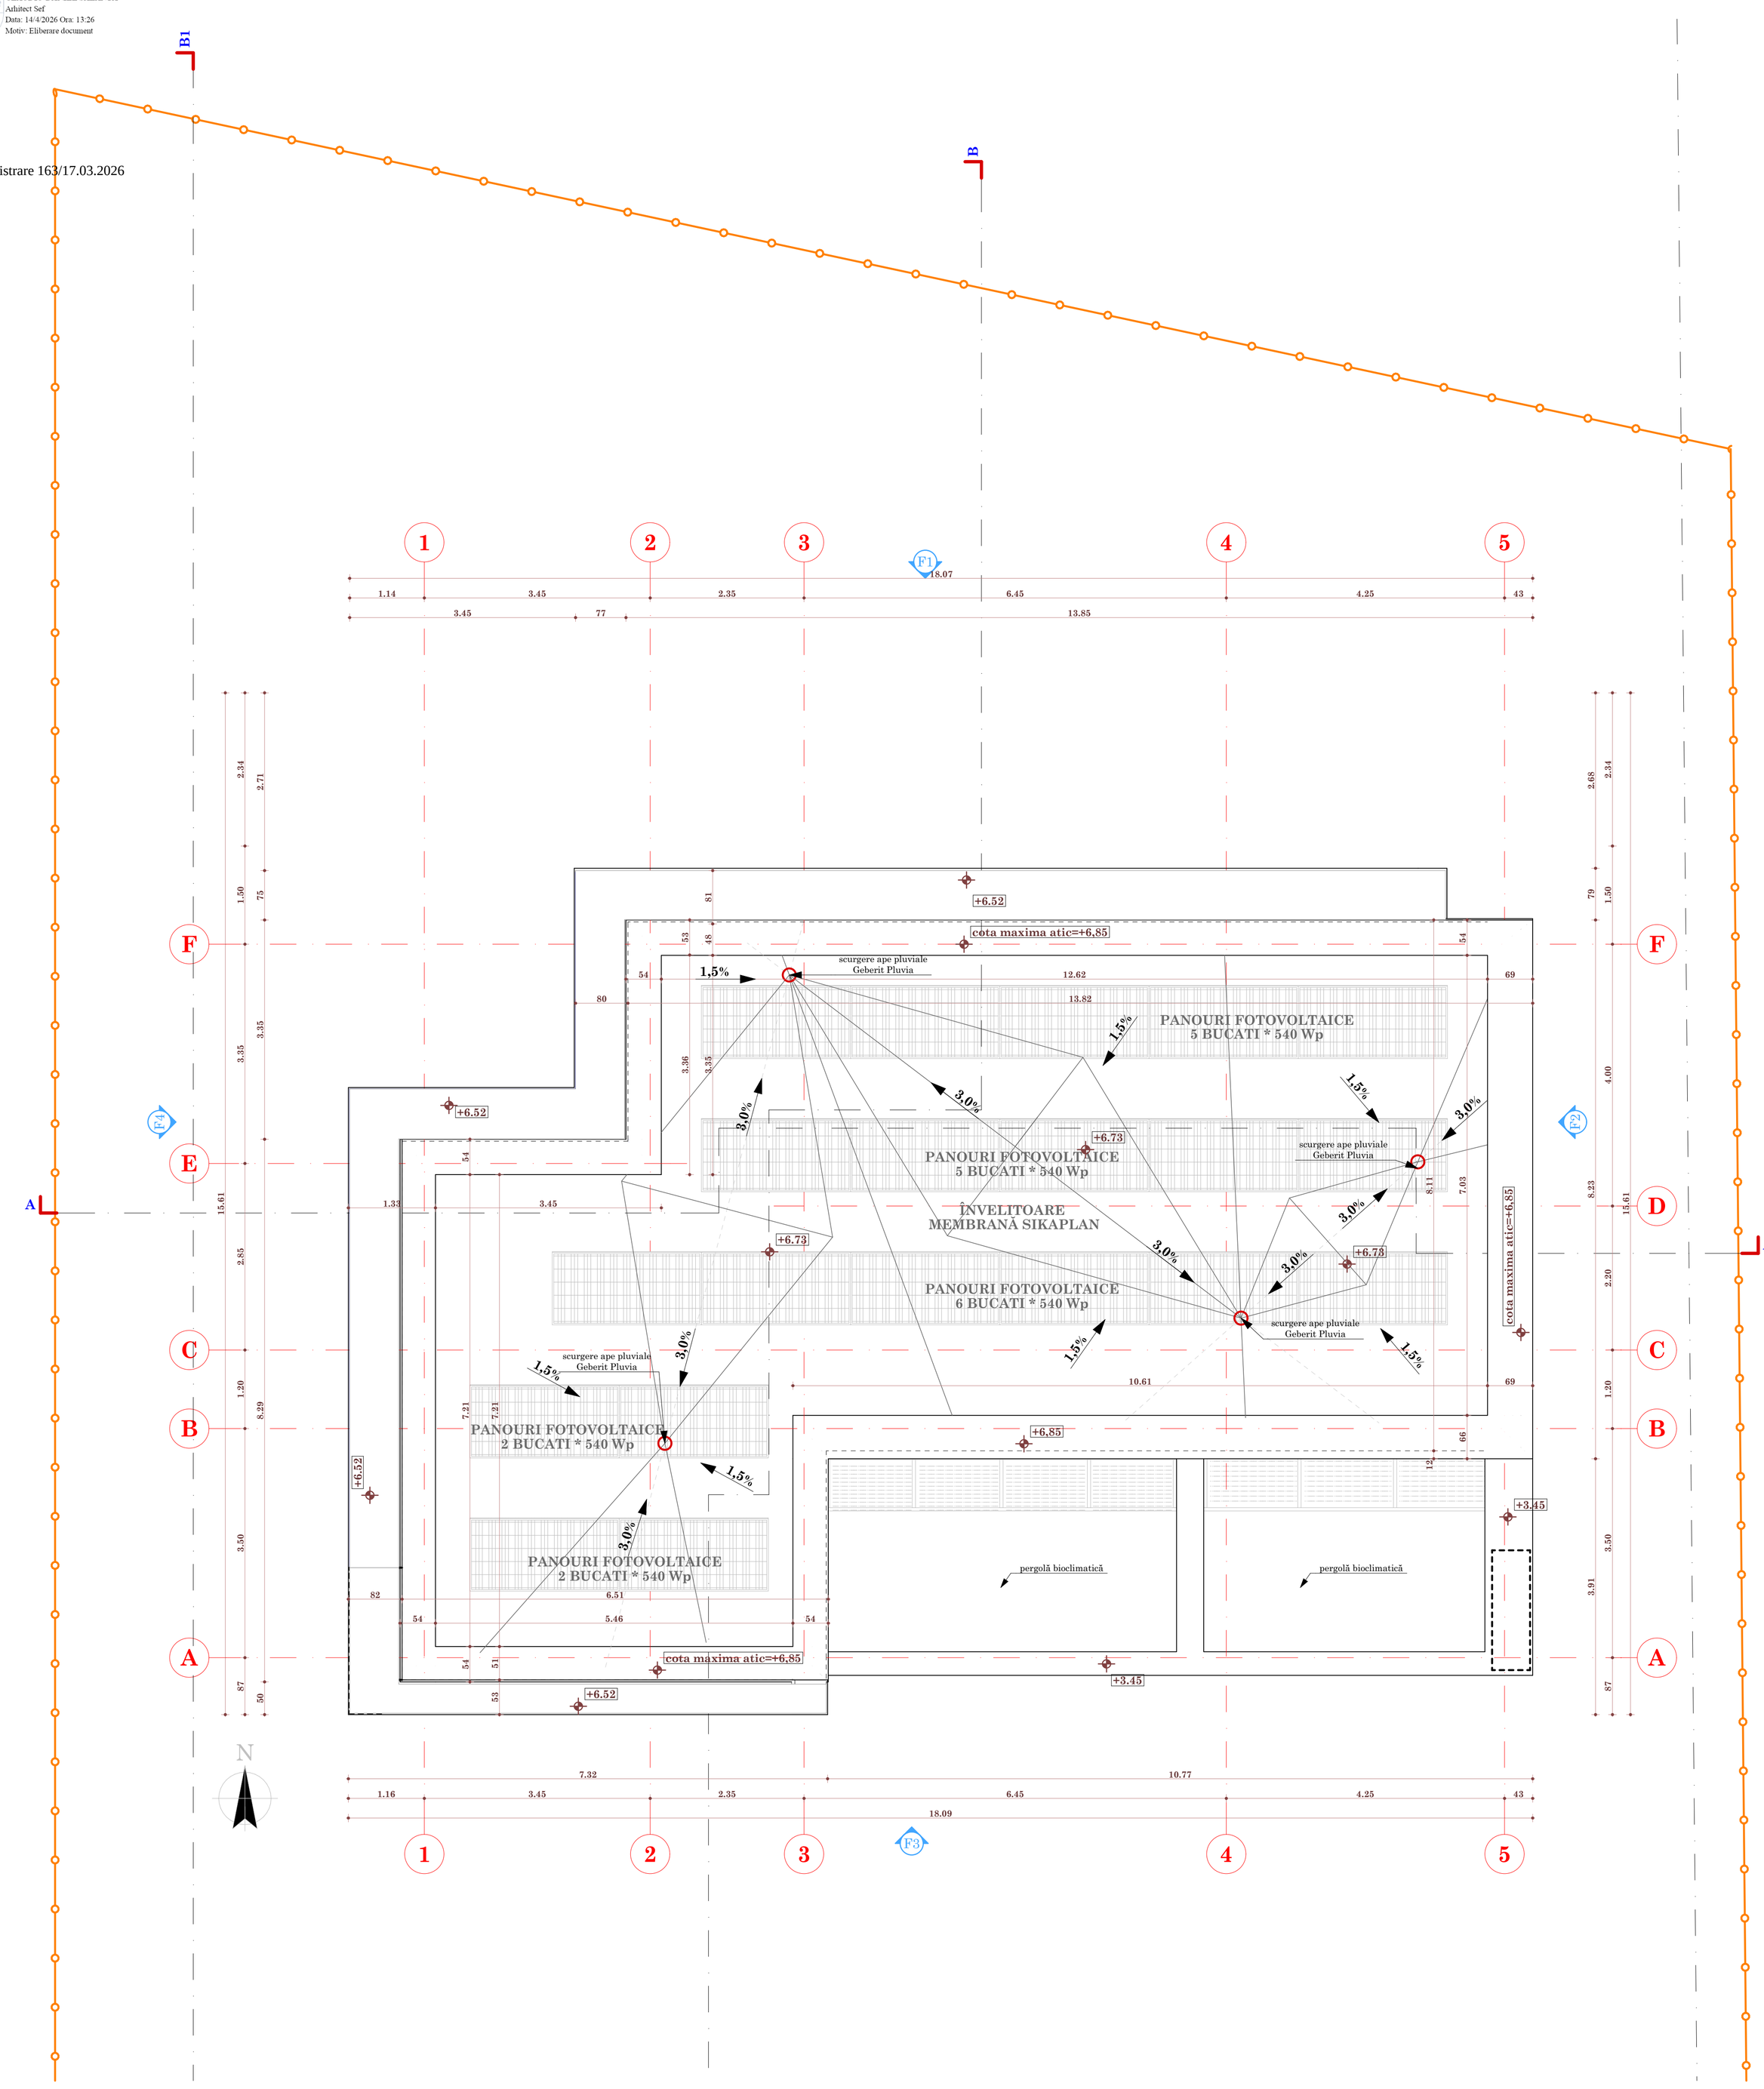

DATE TEHNICE:
Categoria de importanță: C, normal - conform HG 766/97
Clasa de importanță: III - conform P 100-1/2013
Zona seismică: E - conform P100-1/2013 şi SR EN 1988-5/2004
Gradul de rezistență la foc: II - conform NP118/2025
Risc de incendiu: categoria C (risc mic de incendiu)

Szabolcs Hadi
INGINER VERIFICATOR DE PROIECTE; A1,I MDLPA CA V 10559 - semnatura digitala
2026.02.21 10:33:53 +02'00'

VERIFICATOR / EXPERT	NUME	SEMNĂTURA	CERINȚA

UP STUDIO PROJECT
Arhitectura la maximum
RO 29883600, Alba Iulia, jud. Alba, str. Ana Aslan, nr. 29, tel. 0742 068582; www.upstudioproject.com

SPECIFICAȚIE:	TITLU/NUME:	SEMNĂTURA	scara: 1:50
ŞEF PROIECT	Arh. Enacopol Nicoleta		
PROIECTAT	Arh. Razvan Enacopol		data: decembrie 2025
ÎNTOCMIT	Arh. Razvan Carstoi		

BENEFICIAR: DAVID ADRIAN-IOAN SI DAVID ADA-MIHAELA
AMPLASAMENT: jud. CLUJ, comuna Feleacu, sat Feleacu, CF 57673 Feleacu
TITLUL PROIECTULUI: DOCUMENTATIE PT. AUTORIZAREA EXECUTARII LUCRARILOR DE CONSTRUIRE A OBIECTIVULUI <<LOCUINȚĂ UNIFAMILIALĂ ÎMPREJMUIRE ŞI AMENAJĂRI EXTERIOARE>>
TITLUL PLANŞEI: PLAN INVELITOARE

proiect nr.: 245/2024
faza:
format: A1 (59,4 x 84,1 cm)
planşa nr.: A05

Acest desen şi informaţiile cuprinse în el nu pot fi copiate, reproduse sau utilizate, parţial sau în întregime, decât cu acordul scris al UP STUDIO PROJECT şi nu pot fi folosite în alt scop decât cel pentru care au fost elaborate. Planele autentice poartă în original semnătura şi ştampila UP STUDIO PROJECT

2. ÎNVELIOTARE 1:50