
CLAUDIU-DANIEL SALANTA
Arhitect Sef
Data: 14/4/2026 Ora: 13:26
Motiv: Eliberare document

Nr. inregistrare 163/17.03.2026

ENACOPOL ANDONI RAZVAN
2026.02.24 15:13

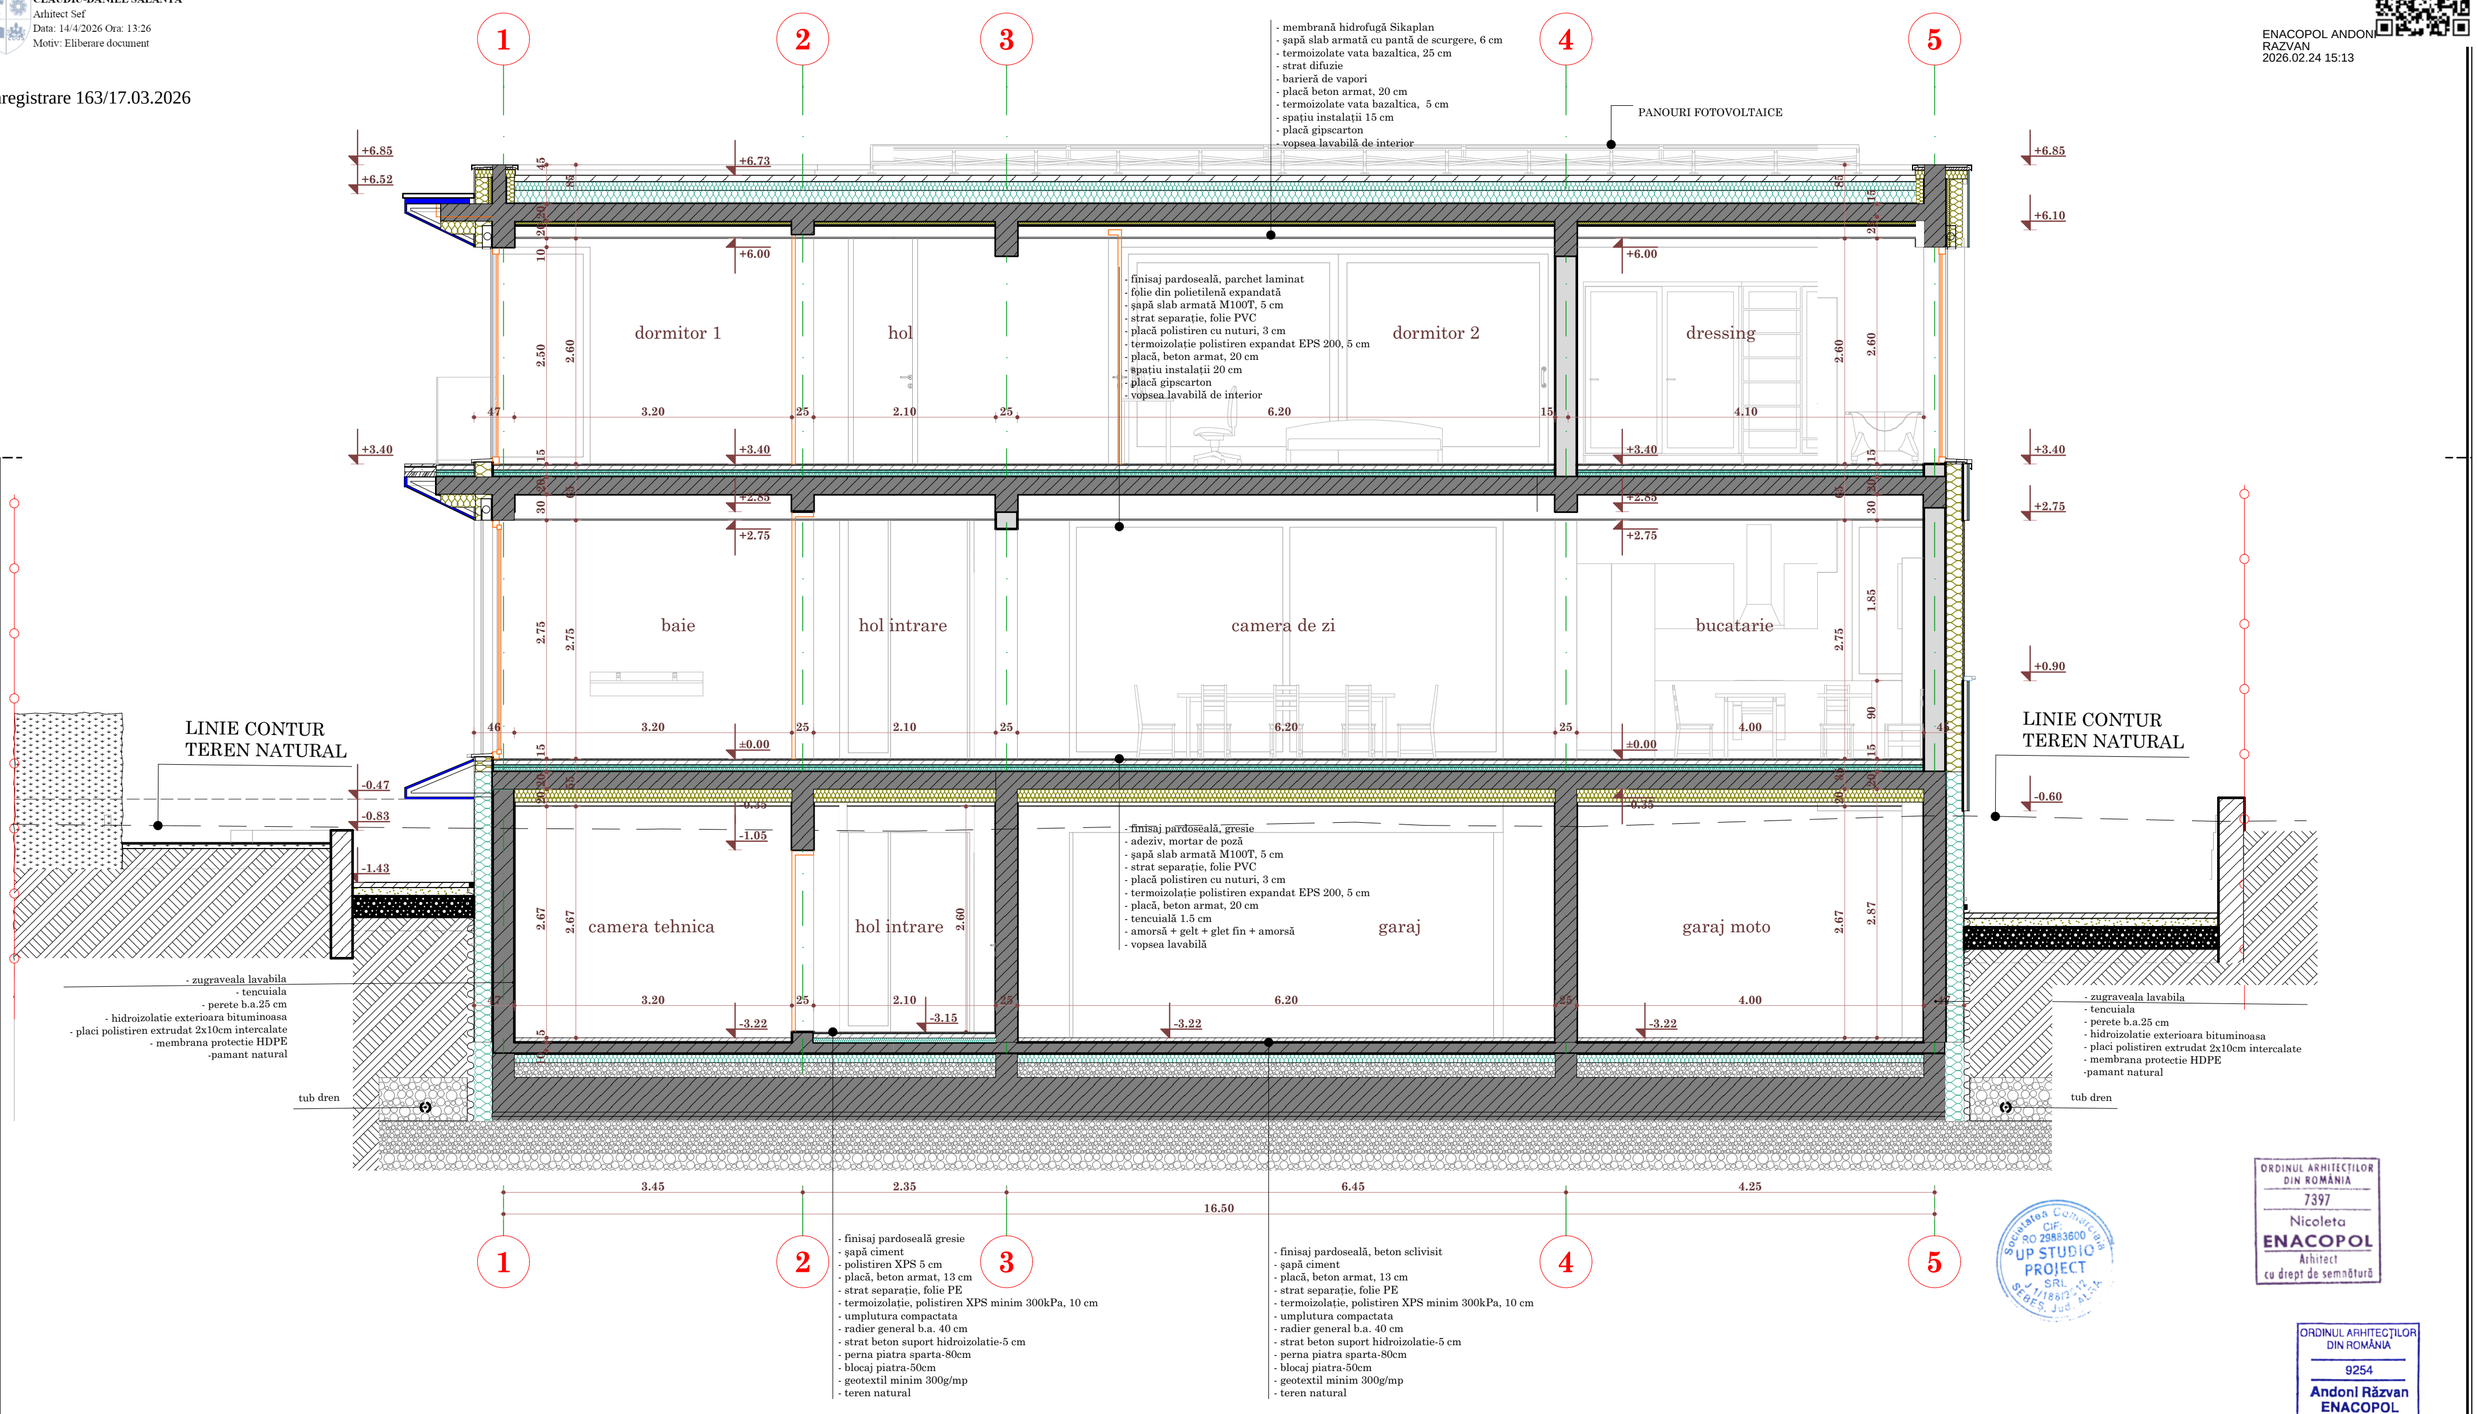

A — Secţiunea A-A — 1:50

DATE TEHNICE:
Categoria de importanţă: C, normal - conform HG 766/97
Clasa de importanţă: III - conform P 100-1/2013
Zona seismică: E - conform P100-1/2013 şi SR EN 1988-5/2004
Gradul de rezistenţă la foc: II - conform NP118/2025
Risc de incendiu: categoria C (risc mic de incendiu)

HADI L. SZABOLCS ROMÂNIA NR. 10559 A1,I INGINER VERIFICATOR DE PROIECTE

Szabolcs Hadi
INGINER VERIFICATOR DE PROIECTE; A1,I MDLPA CA V 10559 - semnatura digitala
2026.02.21 10:34:14 +02'00'

ORDINUL ARHITECTILOR DIN ROMÂNIA 7397 Nicoleta ENACOPOL Arhitect cu drept de semnătură

Societatea Comercială CIF: RO 29883600 UP STUDIO PROJECT SRL J/1188/2026 ALBA

ORDINUL ARHITECŢILOR DIN ROMÂNIA 9254 Andoni Răzvan ENACOPOL Arhitect cu drept de semnătură

VERIFICATOR / EXPERT	NUME	SEMNĂTURA	CERINŢA

UP STUDIO PROJECT
Arhitectura la maltime
RO 29883600, Alba Iulia, jud. Alba, str. Ana Aslan, nr. 29, tel. 0742 068582; www.upstudioproject.com

SPECIFICAŢIE:	TITLU/NUME:	SEMNĂTURA	scara: 1:50
ŞEF PROIECT	Arh. Enacopol Nicoleta		
PROIECTAT	Arh. Razvan Enacopol		data: decembrie 2025
ÎNTOCMIT	Arh. Razvan Carstoi		

BENEFICIAR: DAVID ADRIAN-IOAN SI DAVID ADA-MIHAELA
AMPLASAMENT: jud. CLUJ, comuna Feleacu, sat Feleacu, CF 57673 Feleacu
TITLUL PROIECTULUI: DOCUMENTAŢIE PT. AUTORIZAREA EXECUTARII LUCRARILOR DE CONSTRUIRE A OBIECTIVULUI <<LOCUINŢĂ UNIFAMILIALĂ ÎMPREJMUIRE ŞI AMENAJĂRI EXTERIOARE>>
TITLUL PLANŞEI: SECTIUNE A-A

proiect nr.: 245/2024
faza:
format: A2 59,4 x 42,0 cm
planşa nr.: A06

Acest desen şi informaţiile cuprinse în el nu pot fi copiate, reproduse sau utilizate, parţial sau în întregime, decât cu acordul scris al UP STUDIO PROJECT şi nu pot fi folosite în alt scop decât cel pentru care au fost elaborate. Planele autorizate poartă în original semnătura şi ştampila UP STUDIO PROJECT