
CLAUDIU-DANIEL SALANTA
Arhitect Sef
Data: 14/4/2026 Ora: 13:26
Motiv: Eliberare document

Nr. inregistrare 1637/7.04.2026

ENACOPOL ANDONI RAZVAN
2026.02.24 15:13

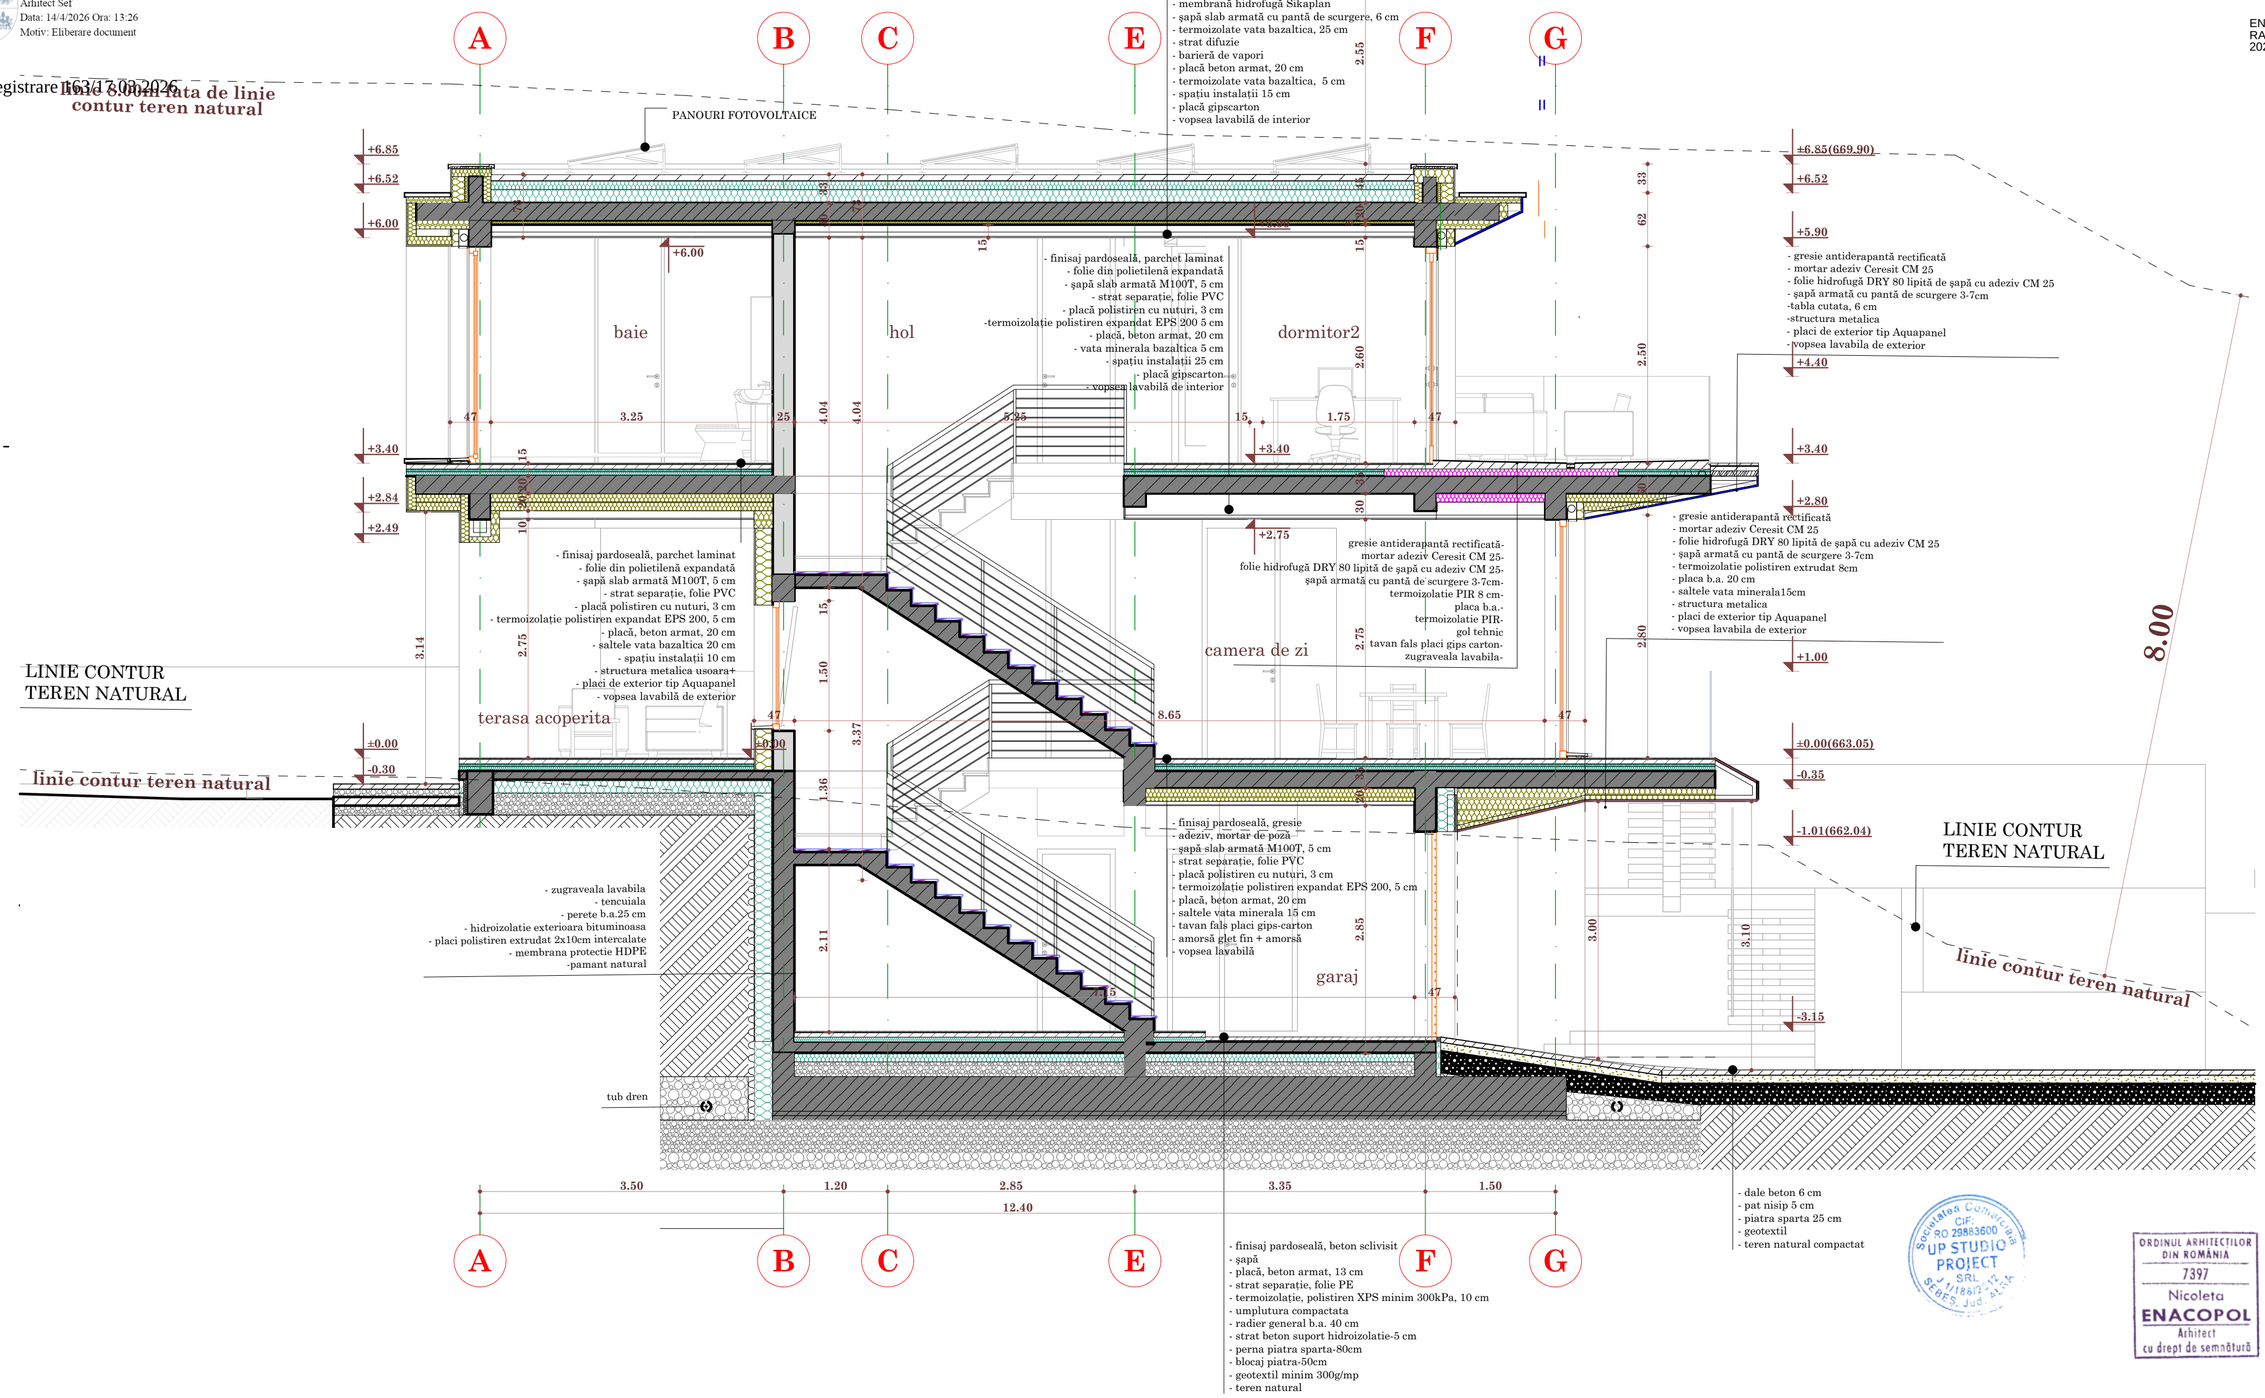

B Secţiunea B-B 1:50

DATE TEHNICE:
Categoria de importanță: C, normal - conform HG 766/97
Clasa de importanță: III - conform P 100-1/2013
Zona seismică: E - conform P100-1/2013 și SR EN 1988-5/2004
Gradul de rezistență la foc: II - conform NP118/2025
Risc de incendiu: categoria C (risc mic de incendiu)

HADUL SZABOLCS ROMÂNIA NR. 10559 A1, I INGINER - VERIFICATOR DE PROIECTE

Szabolcs Hadi
INGINER VERIFICATOR DE PROIECTE; A1,I MDLPA CA V 10559 - semnatura digitala
2026.02.21 10:34:30 +02'00'

VERIFICATOR / EXPERT	NUME	SEMNĂTURA	CERINȚA

UP STUDIO PROJECT
Arhitectura la maxim
RO 29883600, Alba Iulia, jud. Alba, str. Ana Aslan, nr. 29, tel. 0742 068582; www.upstudioproject.com

SPECIFICAȚIE:	TITLU/NUME:	SEMNĂTURA	scara: 1:50
ȘEF PROIECT	Arh. Enacopol Nicoleta		
PROIECTAT	Arh. Razvan Enacopol		data: decembrie 2025
ÎNTOCMIT	Arh. Razvan Carstoi		

BENEFICIAR: DAVID ADRIAN-IOAN SI DAVID ADA-MIHAELA
AMPLASAMENT: jud. CLUJ, comuna Feleacu, sat Feleacu, CF 57673 Feleacu
TITLUL PROIECTULUI: DOCUMENTAȚIE PT. AUTORIZAREA EXECUTARII LUCRARILOR DE CONSTRUIRE A OBIECTIVULUI <<LOCUINȚĂ UNIFAMILIALĂ ÎMPREJMUIRE ȘI AMENAJĂRI EXTERIOARE>>
TITLUL PLANȘEI: SECTIUNE B-B

project nr.: 245/2024
faza:
format: A2 594 x 420 mm
planșa nr.: A07

Acest desen și informațiile cuprinse în el nu pot fi copiate, reproduse sau utilizate, parțial sau în întregime, decât cu acordul scris al UP STUDIO PROJECT și nu pot fi folosite în alt scop decât cel pentru care au fost elaborate. Planșele autorizate poartă în original semnătura și ștampila UP STUDIO PROJECT

Societatea Comercială CIF: RO 29883600 UP STUDIO PROJECT SRL J1/188/2014 SEBEȘ, Jud. ALBA

ORDINUL ARHITECȚILOR DIN ROMÂNIA 7397 Nicoleta ENACOPOL Arhitect cu drept de semnătură

ORDINUL ARHITECȚILOR DIN ROMÂNIA 9254 Andoni Răzvan ENACOPOL Arhitect cu drept de semnătură