

CLAUDIU-DANIEL SALANTA
Arhitect Sef
Data: 14/4/2026 Ora: 13:26
Motiv: Eliberare document

ENACOPOL ANDONI RAZVAN
2026.02.24 15:13

Nr. inregistrare 163/17.03.2026

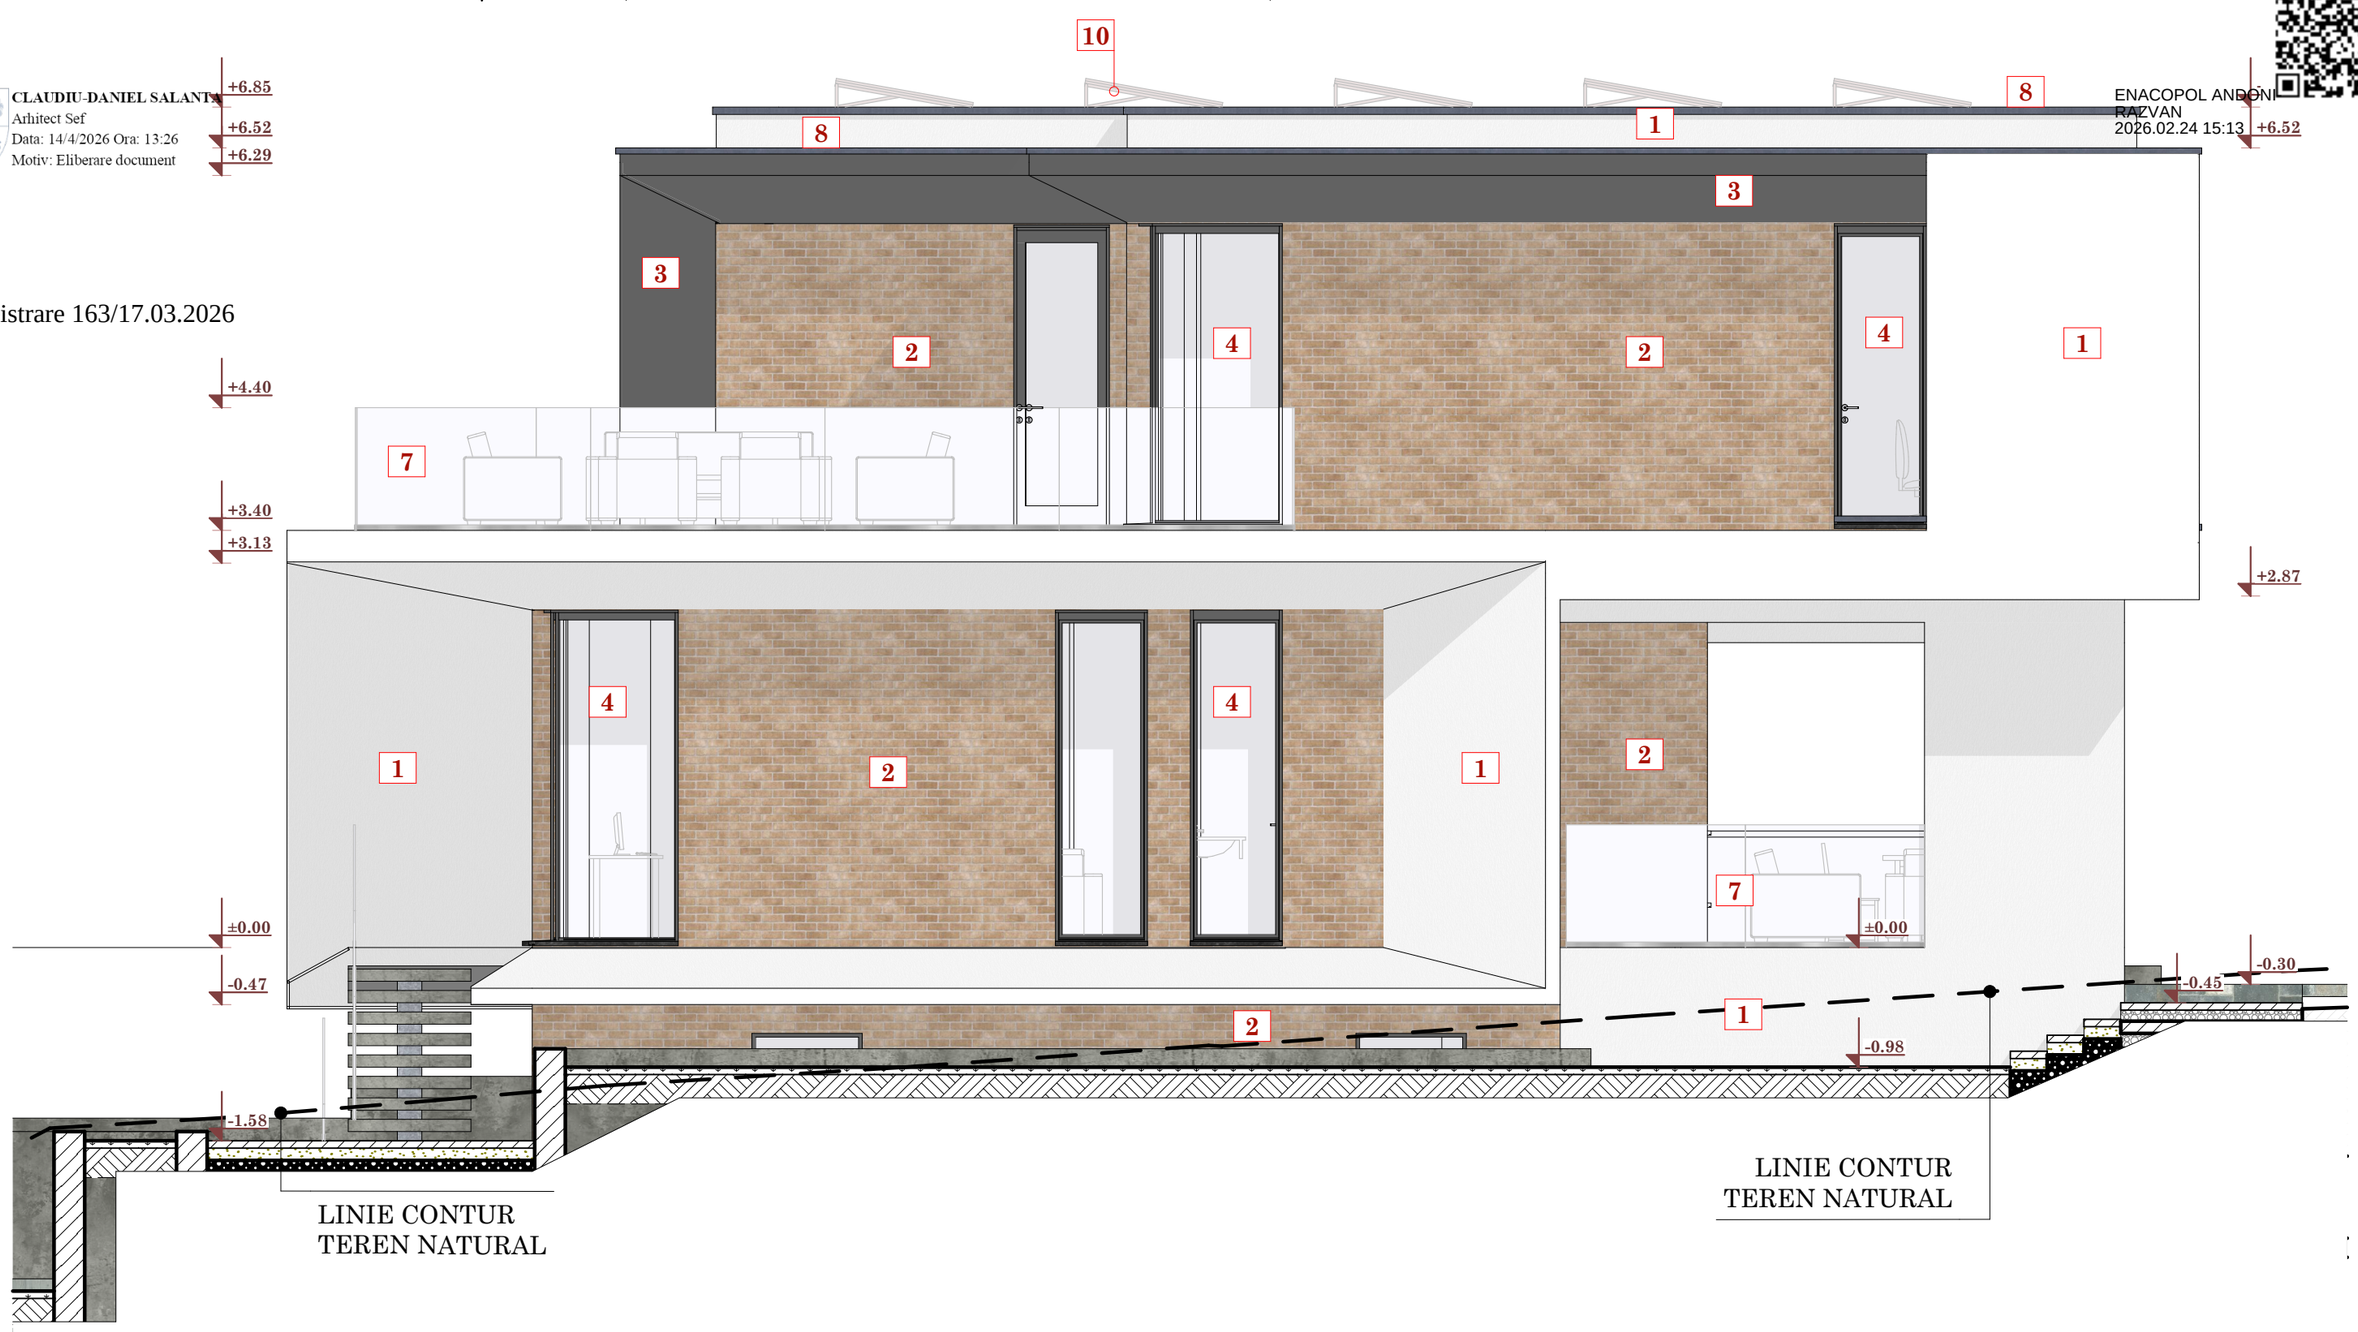

F4 Fațada laterală dreapta 1:50

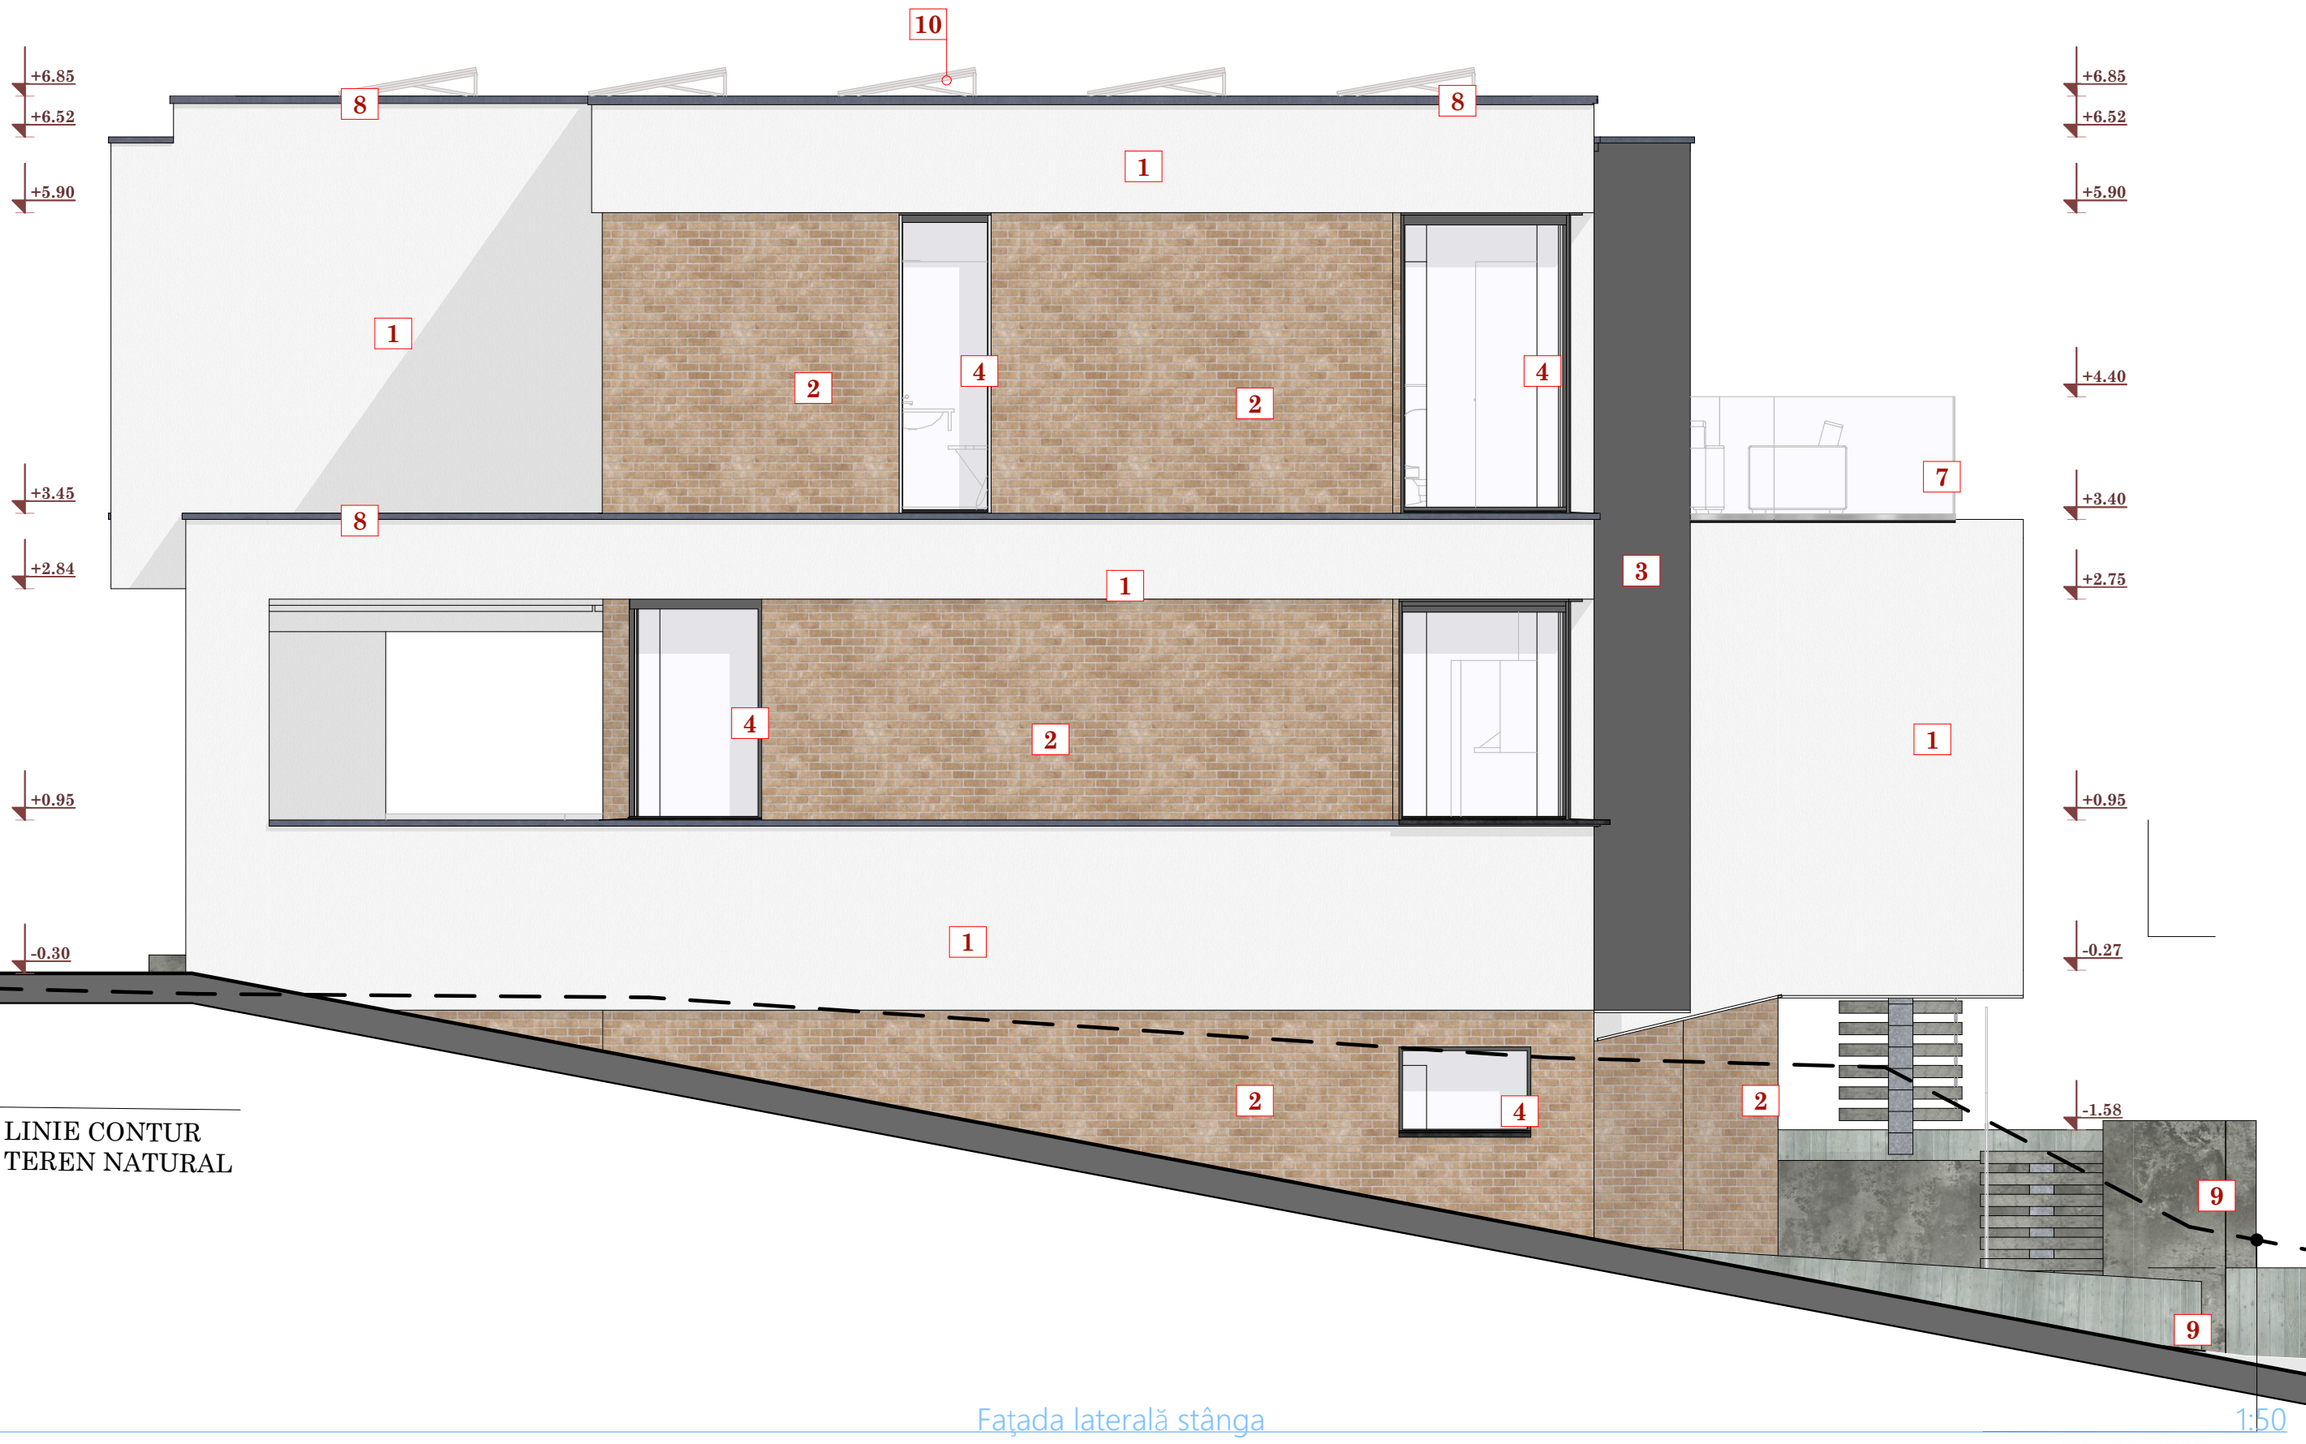

F2 Fațada laterală stânga 1:50

LINIE CONTUR TEREN NATURAL

LEGENDĂ:

1. tencuială decorativă, gran. 1,5 mm, alb RAL9003
2. placare caramida culoare bej-gri
3. placare placi compozit tip Bond culoare gri inchis antracit RAL 7019
4. tâmplărie PVC, gri inchis antracit RAL 7019, geam tripan clar
5. usi intrare lemn stratificat, culoare gri inchis antracit RAL 7019, geam tripan clar
6. usa intrare garaj metalica, culoare gri inchis antracit RAL 7019
7. balustrada sticla clara
8. sort tabla protectie atice- gri inchis antracit RAL 7019
9. parapeti jardiniere finisaj beton aparent
10. panouri fotovoltaice

DATE TEHNICE:

Categoria de importanță: C, normal - conform HG 766/97
Clasa de importanță: III - conform P 100-1/2013
Zona seismică: E - conform P100-1/2013 şi SR EN 1988-5/2004
Gradul de rezistență la foc: II - conform NP118/2025
Risc de incendiu: categoria C (risc mic de incendiu)

Societatea Comercială CIF: RO 29883600 UP STUDIO PROJECT SRL J1/1888/2024 SEBEŞ, Jud. ALBA

ORDINUL ARHITECȚILOR DIN ROMÂNIA 7397 Nicoleta ENACOPOL Arhitect cu drept de semnătură

ORDINUL ARHITECȚILOR DIN ROMÂNIA 9254 Andoni Răzvan ENACOPOL Arhitect cu drept de semnătură

VERIFICATOR / EXPERT	NUME	SEMNĂTURA	CERINȚA

UP STUDIO PROJECT
Arhitectura la maltime
RO 29883600, Alba Iulia, jud. Alba, str. Ana Aslan, nr. 29, tel. 0742 068582; www.upstudioproject.com

SPECIFICAȚIE:	TITLU/NUME:	SEMNĂTURA	scara: 1:50
ŞEF PROIECT	Arh. Enacopol Nicoleta		
PROIECTAT	Arh. Razvan Enacopol		data: decembrie 2025
ÎNTOCMIT	Arh. Razvan Carstoi		

BENEFICIAR: DAVID ADRIAN-IOAN SI DAVID ADA-MIHAELA
AMPLASAMENT: jud. CLUJ, comuna Feleacu, sat Feleacu, CF 57673 Feleacu
TITLUL PROIECTULUI: DOCUMENTAȚIE PT. AUTORIZAREA EXECUTARII LUCRARILOR DE CONSTRUIRE A OBIECTIVULUI <<LOCUINȚĂ UNIFAMILIALĂ ÎMPREJMUIRE ŞI AMENAJĂRI EXTERIOARE>>
TITLUL PLANŞEI: FATADA LATERALA STANGA SI DREAPTA

proiect nr.: 245/2024
faza:
format: A2 42,0 x 59,4 cm
planșa nr.: A10

Acest desen şi informațiile cuprinse in el nu pot fi copiate, reproduse sau utilizate, partial sau in intregime, decât cu acordul scris al UP STUDIO PROJECT şi nu pot fi folosite în alt scop decât cel pentru care au fost elaborate. Planele autentice poartă în original semnătura şi ştampila UP STUDIO PROJECT.