

CLAUDIU-DANIEL SALANTA
Arhitect Sef
Data: 11/4/2026 Ora: 13:26
Motiv: Eliberare document
Nr. inregistrare 163/17.03.2026


ENACOPOL ANDONI RAZVAN
2026.02.24 15:13

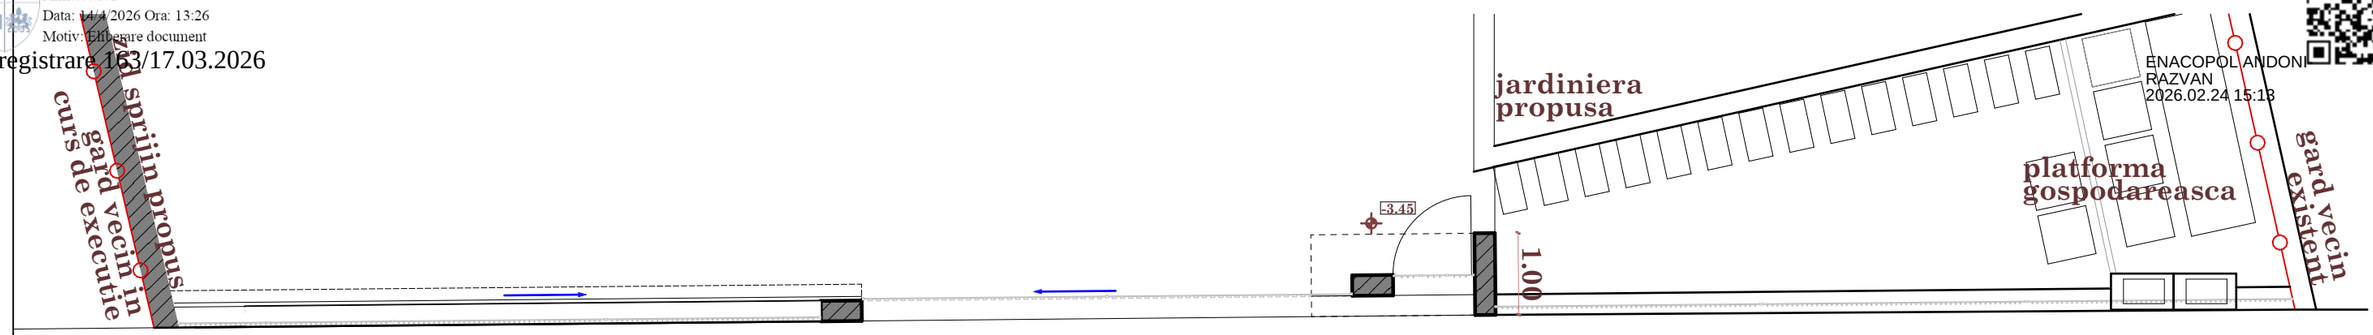

PLAN

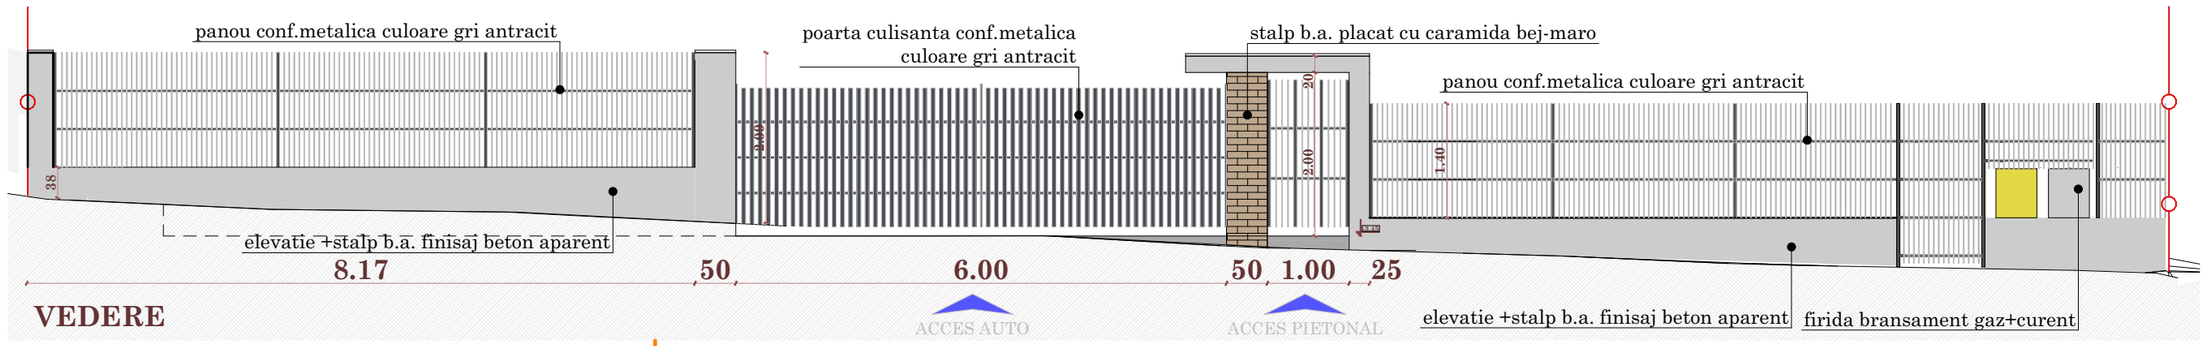

VEDERE

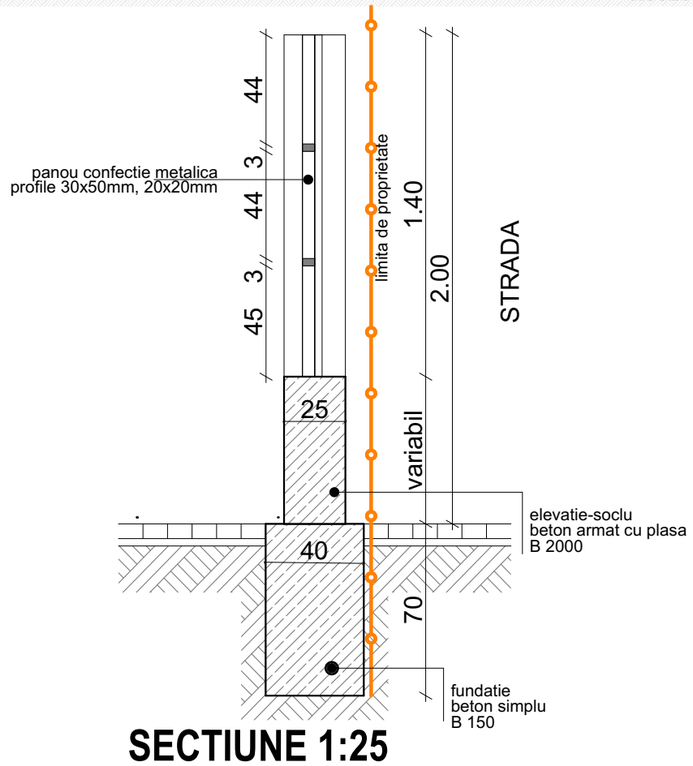

SECTIUNE 1:25

Societatea Comerciala CIF: RO 29883600 UP STUDIO PROJECT SRL J1/1881/2012 SEBES, Jud. ALBA

ORDINUL ARHITECȚILOR DIN ROMÂNIA
7397
Nicoleta
ENACOPOL
Arhitect
cu drept de semnătură

ORDINUL ARHITECȚILOR DIN ROMÂNIA
9254
Andoni Răzvan
ENACOPOL
Arhitect cu drept de semnătură

VERIFICATOR / EXPERT	NUME	SEMNĂTURA	CERINȚA

UP STUDIO PROJECT
Arhitectura la maltime
RO 29883600, Alba Iulia, jud. Alba, str. Ana Aslan, nr. 29, tel. 0742 068582; www.upstudioproject.com

SPECIFICAȚIE:	TITLU/NUME:	SEMNĂTURA
SEF PROIECT	Arh. Nicoleta Enacopol	
PROIECTAT	Arh. Razvan Enacopol	
ÎNTOCMIT	Arh. Razvan Carstoi	

scara:
data: decembrie 2025

BENEFICIAR: DAVID ADRIAN-IOAN SI DAVID ADA-MIHAELA
AMPLASAMENT: jud. CLUJ, comuna Feleacu, sat Feleacu, CF 57673 Feleacu

TITLUL PROIECTULUI: DOCUMENTAȚIE PT. AUTORIZAREA EXECUTARII LUCRARILOR DE CONSTRUIRE A OBIECTIVULUI <<LOCUINȚĂ UNIFAMILIALĂ ÎMPREJMUIRE ȘI AMENAJĂRI EXTERIOARE>>

TITLUL PLANȘEI: IMPREJMUIRE TIP 1

proiect nr.: 245/2024
faza: D.T.A.C.
format: A3 42,0 x 29,7 cm
planșa nr.: A11

Acest desen și informațiile cuprinse în el nu pot fi copiate, reproduse sau utilizate, parțial sau în întregime, decât cu acordul scris al UP STUDIO PROJECT și nu pot fi folosite în alt scop decât cel pentru care au fost elaborate. Planșele autentice poartă în original semnătura și ștampila UP STUDIO PROJECT